Grundriss / Draufsicht

UX-TEST 28.10.2026 · Büro · Bad

Entwurf · Intern · Revision 5

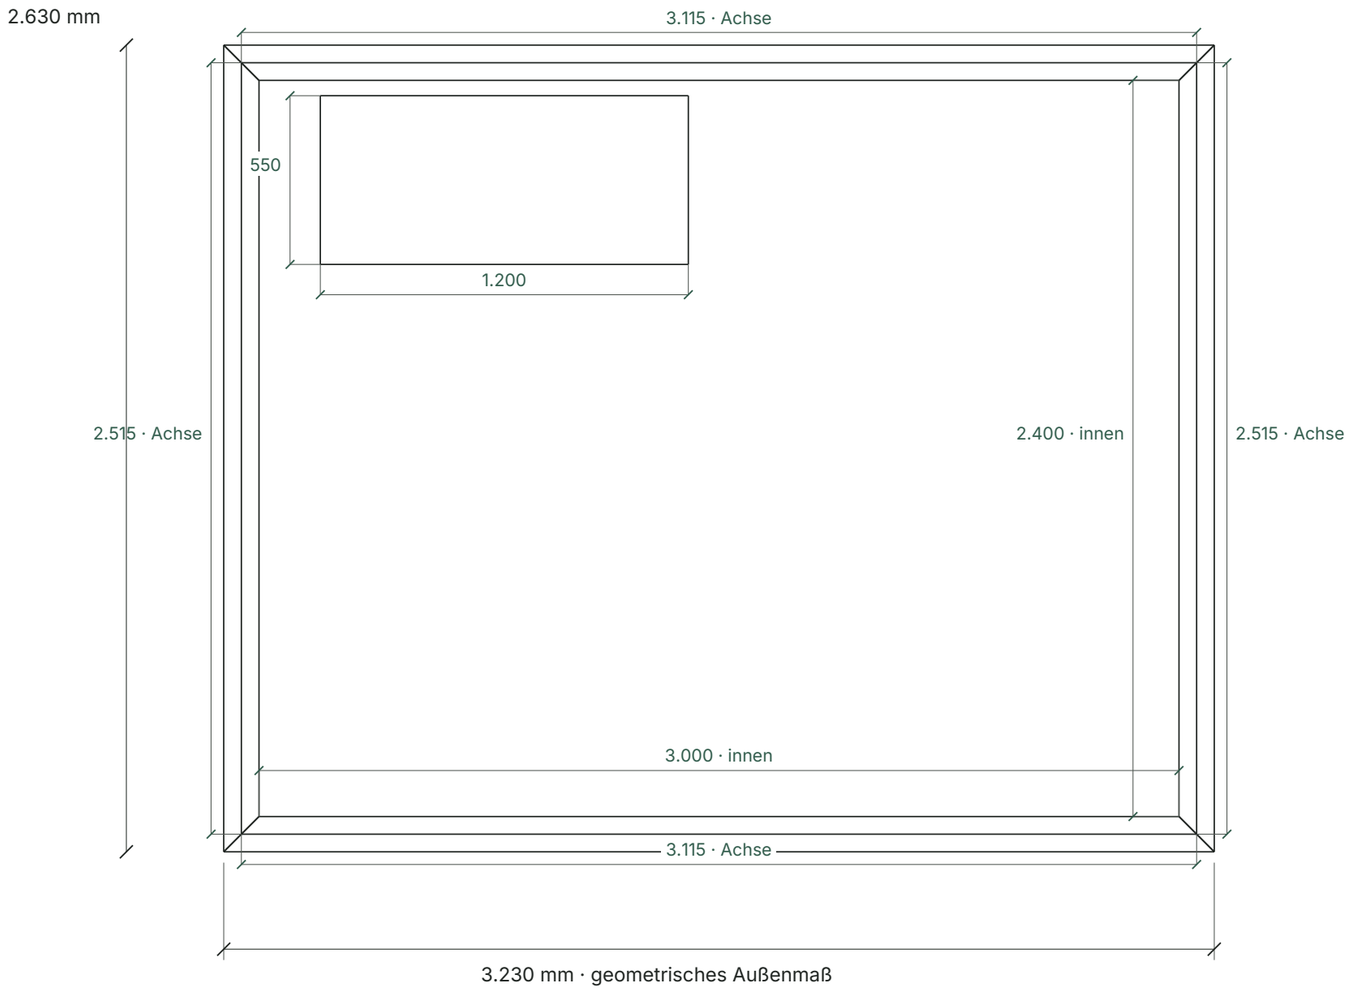

282,22 mm · Maßstab 1:20

Höhenbezug: Planursprung · Höhenbezug noch zu bestätigen

Maße in mm. „Achse“ bezeichnet die Wandachse; „innen“ das modellierte lichte Innenmaß. Planmaße sind kein bestätigtes Aufmaß. Wandaufbau und Einbaumaße vor Ort prüfen. Speicherpräzision 0,01 mm ist keine Fertigungstoleranz.

Modellhash 96230c68773a2ca05ce0371b5a24003251c4e3f63f620b40090a107161e5b775

Vorderansicht

UX-TEST 28.10.2026 · Büro · Bad

Entwurf · Intern · Revision 5

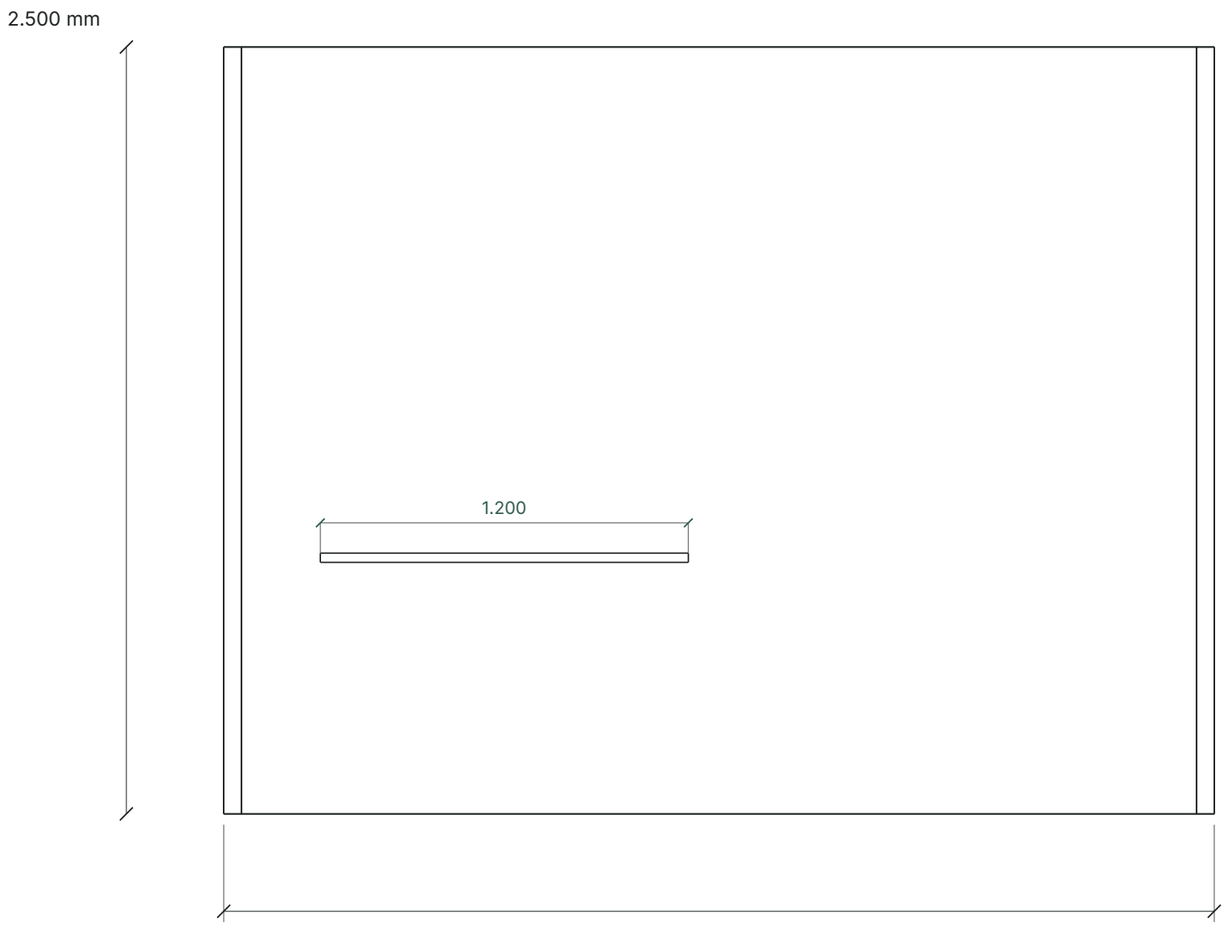

282,22 mm · Maßstab 1:20

Höhenbezug: Planursprung · Höhenbezug noch zu bestätigen

Maße in mm. „Achse“ bezeichnet die Wandachse; „innen“ das modellierte lichte Innenmaß. Planmaße sind kein bestätigtes Aufmaß. Wandaufbau und Einbaumaße vor Ort prüfen. Speicherpräzision 0,01 mm ist keine Fertigungstoleranz.

Modellhash 96230c68773a2ca05ce0371b5a24003251c4e3f63f620b40090a107161e5b775

Seitenansicht

UX-TEST 28.10.2026 · Büro · Bad

Entwurf · Intern · Revision 5

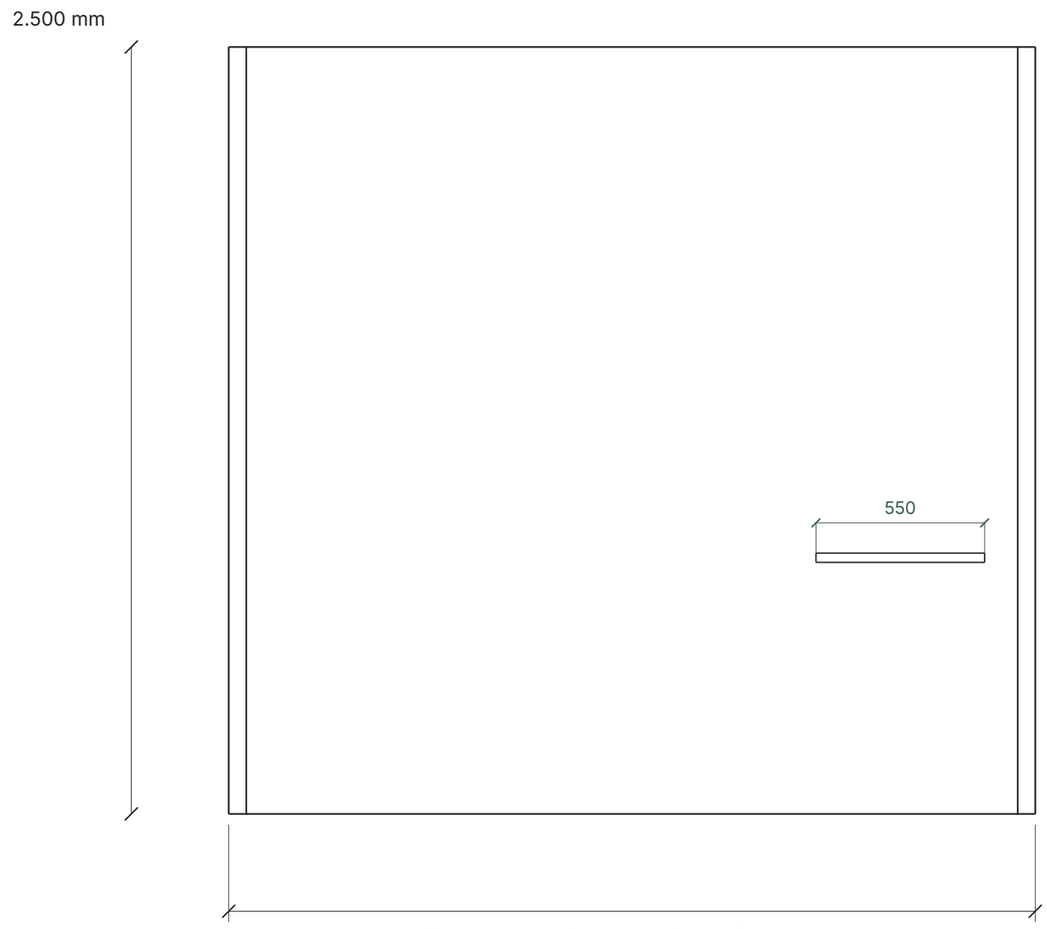

282,22 mm · Maßstab 1:20

Höhenbezug: Planursprung · Höhenbezug noch zu bestätigen

Maße in mm. „Achse“ bezeichnet die Wandachse; „innen“ das modellierte lichte Innenmaß. Planmaße sind kein bestätigtes Aufmaß. Wandaufbau und Einbaumaße vor Ort prüfen. Speicherpräzision 0,01 mm ist keine Fertigungstoleranz.

Modellhash 96230c68773a2ca05ce0371b5a24003251c4e3f63f620b40090a107161e5b775

Stück- und Bearbeitungsliste

UX-TEST 28.10.2026 · Büro · Bad

Entwurf · Intern · Revision 5

BAUTEIL / AUSFÜHRUNG	MENGE	EINHEIT
TEST Bad Büro · Wand 1 Wand · Stärke 115 mm · Netto 7,7875 m² · Volumen 0,8955625 m³	3,115	m
TEST Bad Büro · Wand 2 Wand · Stärke 115 mm · Netto 6,2875 m² · Volumen 0,7230625 m³	2,515	m
TEST Bad Büro · Wand 3 Wand · Stärke 115 mm · Netto 7,7875 m² · Volumen 0,8955625 m³	3,115	m
TEST Bad Büro · Wand 4 Wand · Stärke 115 mm · Netto 6,2875 m² · Volumen 0,7230625 m³	2,515	m
TEST Bad Büro Raumfläche · Flächenbezug: Wandachsen, kein lichtes Innenmaß · Achsfläche 7,834225 m² · Umfang zwischen Wandachsen 11,26 m	7,834225	m²
TEST Waschtischplatte Natursteinbauteil · Materialstand: noch nicht zugeordnet / Bezeichnung nicht verfügbar · Stärke 30 mm · Netto 0,66 m² · Volumen 0,0198 m³ · Bearbeitete Kante 0 m	1	Stk

Mengen entstehen aus dieser Revision. Kein pauschaler Verschnitt, keine erfundenen Einkaufsdaten, keine Gewichtsannahme ohne belegte Materialdichte. Modellierte Ausschnitte werden explizit abgezogen. Flächenregeln für die Abrechnung separat fachlich bestätigen.

Modellhash 96230c68773a2ca05ce0371b5a24003251c4e3f63f620b40090a107161e5b775

- „TEST Bad Büro · Wand 1“: Dieses Maß (2500 mm) ist als Planmaß eingetragen, aber noch nicht fachlich bestätigt.
- „TEST Bad Büro · Wand 1“: Dieses Maß (115 mm) ist als Planmaß eingetragen, aber noch nicht fachlich bestätigt.
- „TEST Bad Büro · Wand 2“: Dieses Maß (2500 mm) ist als Planmaß eingetragen, aber noch nicht fachlich bestätigt.
- „TEST Bad Büro · Wand 2“: Dieses Maß (115 mm) ist als Planmaß eingetragen, aber noch nicht fachlich bestätigt.
- „TEST Bad Büro · Wand 3“: Dieses Maß (2500 mm) ist als Planmaß eingetragen, aber noch nicht fachlich bestätigt.
- „TEST Bad Büro · Wand 3“: Dieses Maß (115 mm) ist als Planmaß eingetragen, aber noch nicht fachlich bestätigt.
- „TEST Bad Büro · Wand 4“: Dieses Maß (2500 mm) ist als Planmaß eingetragen, aber noch nicht fachlich bestätigt.
- „TEST Bad Büro · Wand 4“: Dieses Maß (115 mm) ist als Planmaß eingetragen, aber noch nicht fachlich bestätigt.
- „TEST Bad Büro“: Dieses Maß (0 mm) ist als Planmaß eingetragen, aber noch nicht fachlich bestätigt.
- „TEST Waschtischplatte · Länge“: Länge (1200 mm) ist als Planmaß eingetragen, aber noch nicht fachlich bestätigt.
- „TEST Waschtischplatte · Tiefe“: Tiefe (550 mm) ist als Planmaß eingetragen, aber noch nicht fachlich bestätigt.
- „TEST Waschtischplatte“: konkrete Materialversion fehlt.
- „TEST Waschtischplatte“: Stärke (30 mm) ist als Planmaß eingetragen, aber noch nicht fachlich bestätigt.
- „TEST Waschtischplatte“: vorgesehenes Rohmaß oder konkrete Rohplatte und Zuschnittbezug sind noch offen.
- Geometrieprüfung ersetzt keine Prüfung von Untergrund, Abdichtung, Materialeignung, Lasten oder Einbausituation.

Modellhash 96230c68773a2ca05ce0371b5a24003251c4e3f63f620b40090a107161e5b775