Grundriss / Draufsicht

UX Nachtest planner_a · Innenmaße Raum

Entwurf · Intern · Revision 3

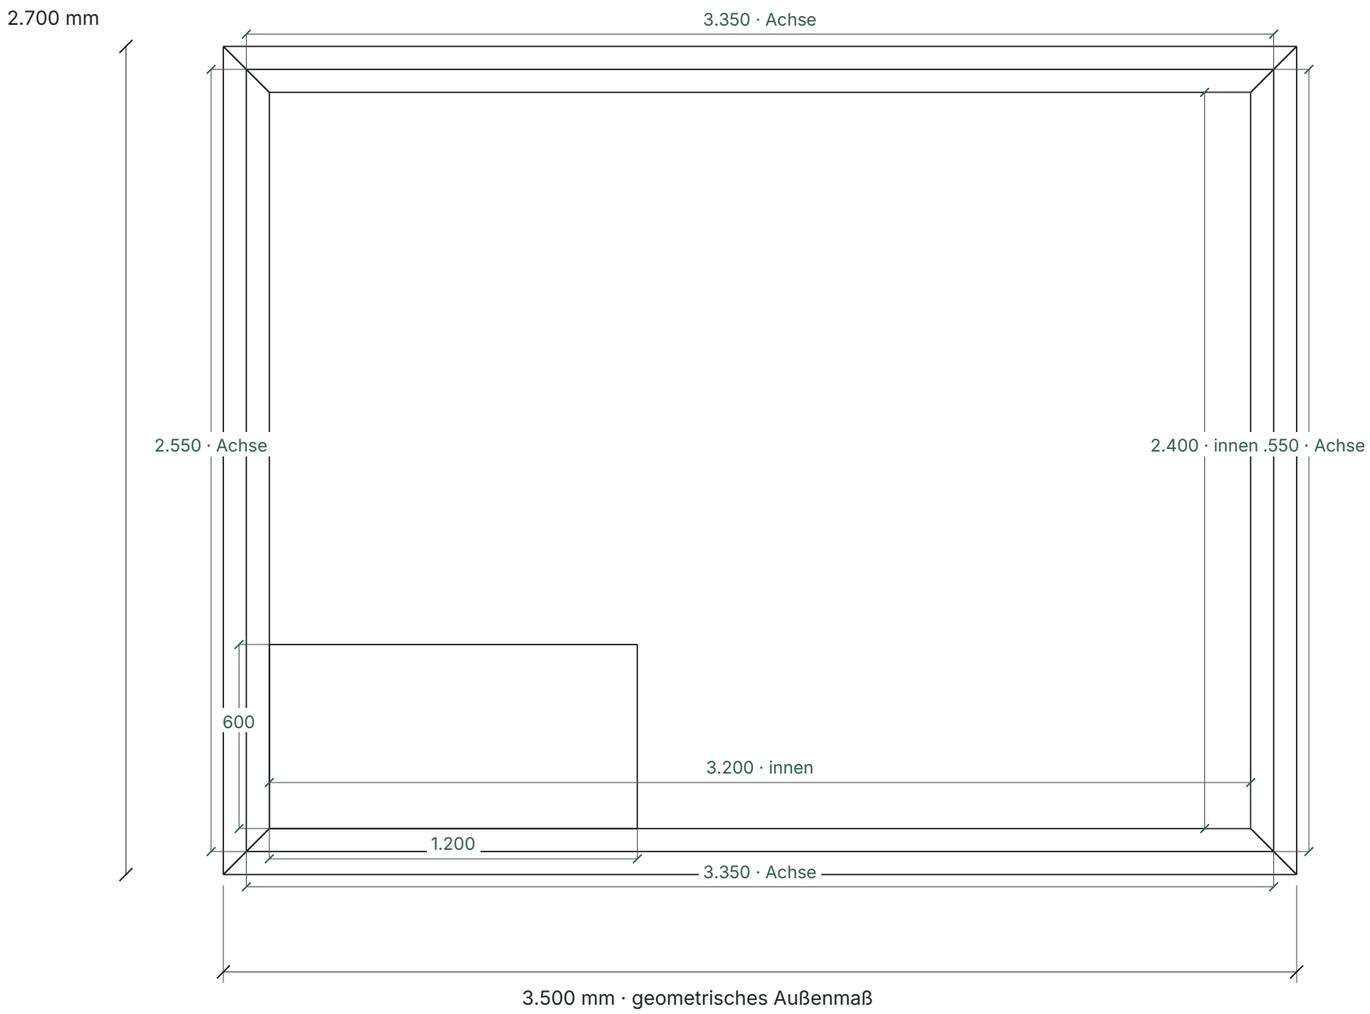

282,22 mm · Maßstab 1:20

Höhenbezug: Planursprung · Höhenbezug noch zu bestätigen

Maße in mm. „Achse“ bezeichnet die Wandachse; „innen“ das modellierte lichte Innenmaß. Planmaße sind kein bestätigtes Aufmaß. Wandaufbau und Einbaumaße vor Ort prüfen. Speicherpräzision 0,01 mm ist keine Fertigungstoleranz.

Modellhash 54e80a856ce3bda9459534e770f988db91b14ffeafff3fedc5e4f4b7428a922c

Vorderansicht

UX Nachtest planner_a · Innenmaße Raum

Entwurf · Intern · Revision 3

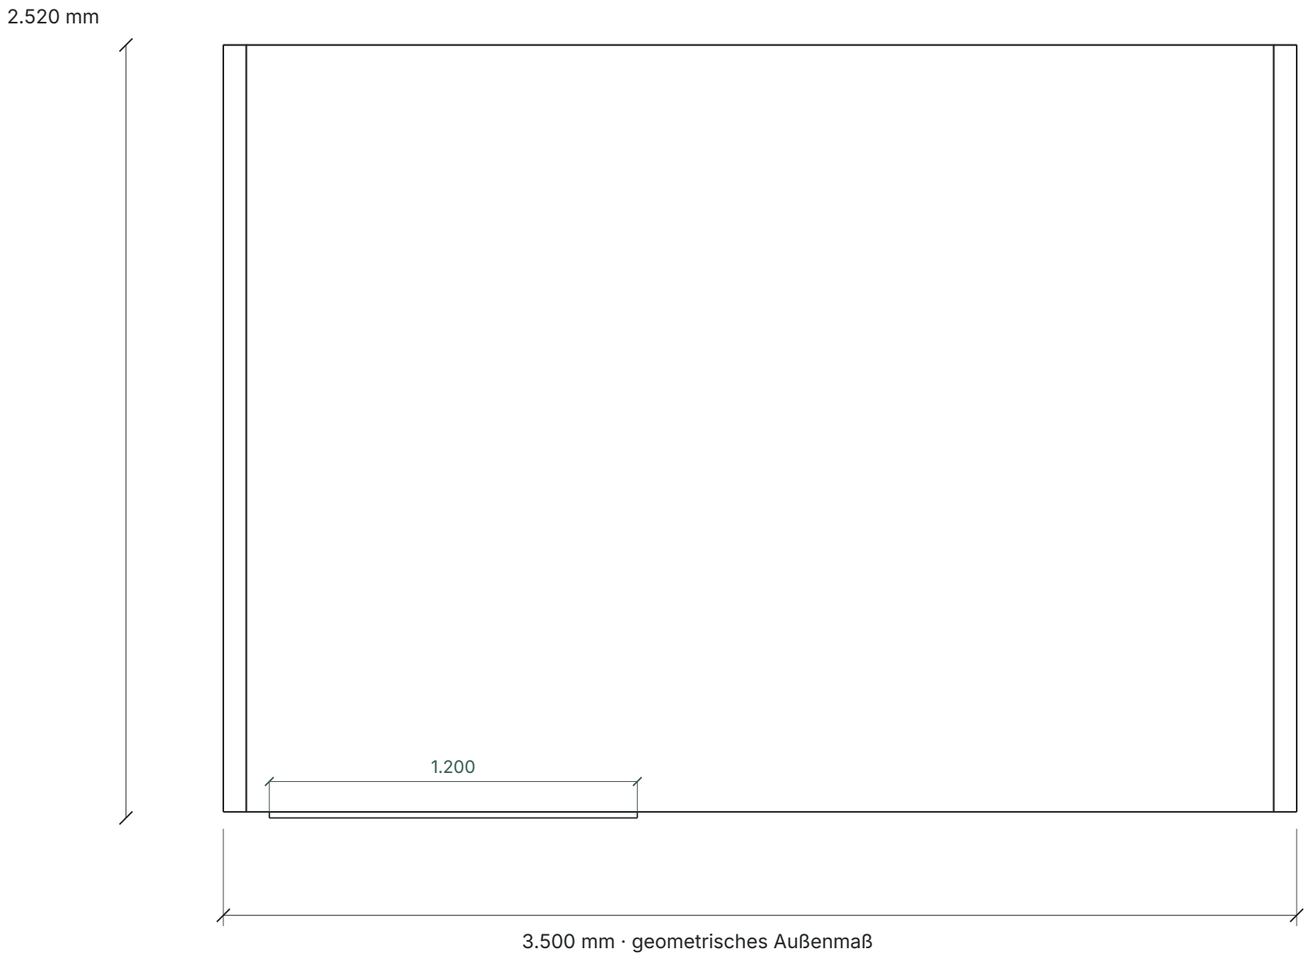

282,22 mm · Maßstab 1:20

Höhenbezug: Planursprung · Höhenbezug noch zu bestätigen

Maße in mm. „Achse“ bezeichnet die Wandachse; „innen“ das modellierte lichte Innenmaß. Planmaße sind kein bestätigtes Aufmaß. Wandaufbau und Einbaumaße vor Ort prüfen. Speicherpräzision 0,01 mm ist keine Fertigungstoleranz.

Modellhash 54e80a856ce3bda9459534e770f988db91b14ffeafff3fedc5e4f4b7428a922c

Seitenansicht

UX Nachtest planner_a · Innenmaße Raum

Entwurf · Intern · Revision 3

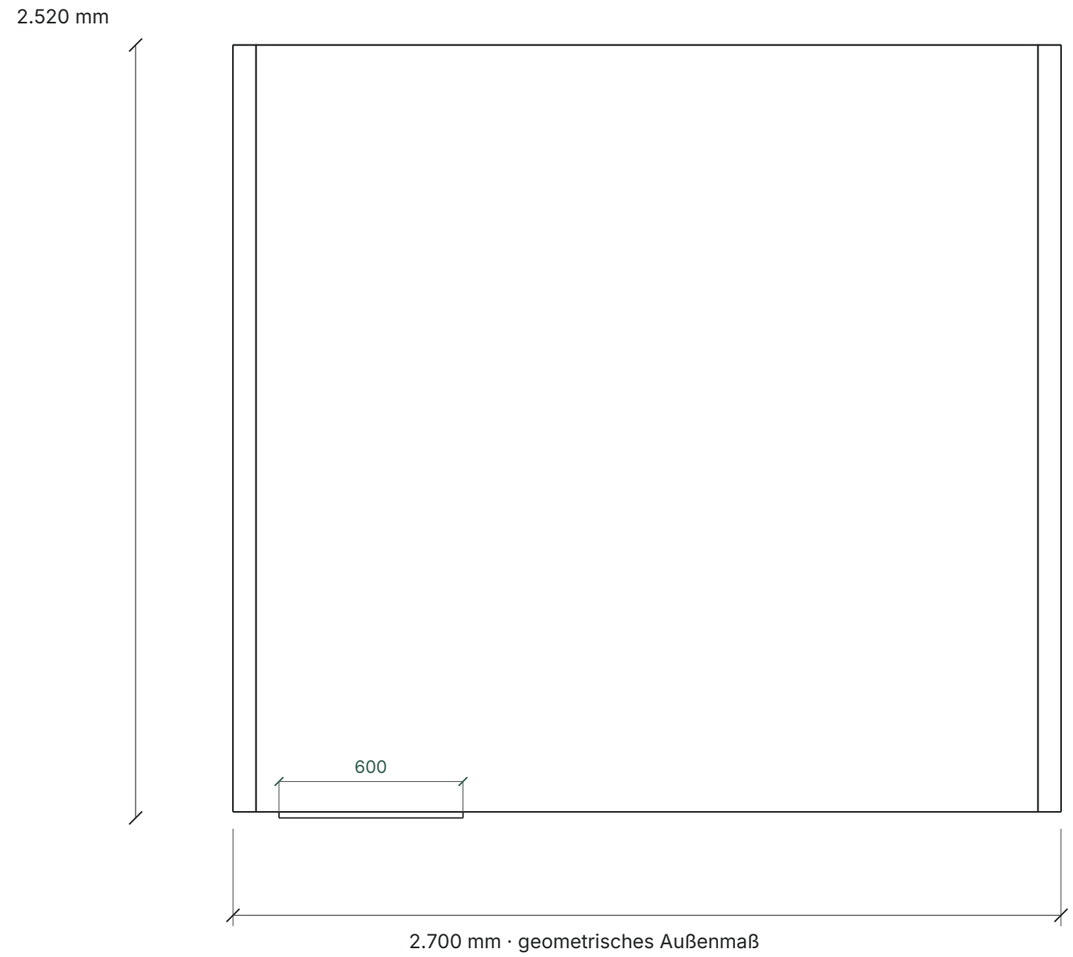

282,22 mm · Maßstab 1:20

Höhenbezug: Planursprung · Höhenbezug noch zu bestätigen

Maße in mm. „Achse“ bezeichnet die Wandachse; „innen“ das modellierte lichte Innenmaß. Planmaße sind kein bestätigtes Aufmaß. Wandaufbau und Einbaumaße vor Ort prüfen. Speicherpräzision 0,01 mm ist keine Fertigungstoleranz.

Modellhash 54e80a856ce3bda9459534e770f988db91b14ffeafff3fedc5e4f4b7428a922c

Stück- und Bearbeitungsliste

UX Nachtest planner_a · Innenmaße Raum

Entwurf · Intern · Revision 3

BAUTEIL / AUSFÜHRUNG	MENGE	EINHEIT
UX Nachtest planner_a · Innenraum · Wand 1 Wand · Stärke 150 mm · Netto 8,375 m² · Volumen 1,25625 m³	3,35	m
UX Nachtest planner_a · Innenraum · Wand 2 Wand · Stärke 150 mm · Netto 6,375 m² · Volumen 0,95625 m³	2,55	m
UX Nachtest planner_a · Innenraum · Wand 3 Wand · Stärke 150 mm · Netto 8,375 m² · Volumen 1,25625 m³	3,35	m
UX Nachtest planner_a · Innenraum · Wand 4 Wand · Stärke 150 mm · Netto 6,375 m² · Volumen 0,95625 m³	2,55	m
UX Nachtest planner_a · Innenraum Raumfläche · Flächenbezug: Wandachsen, kein lichtes Innenmaß · Achsfläche 8,5425 m² · Umfang zwischen Wandachsen 11,8 m	8,5425	m²
UX Nachtest planner_a · Waschtisch Natursteinbauteil · Materialstand: BIANCO SARDO · Katalogreferenz · Version 1 · Katalog: rossittis-public-2026-10-19-v1 · Herstellerquelle: https://rossittis.de/material/sardo-bianco · Quellenprüfung: 2026-10-19 · Stärke 20 mm · Netto 0,72 m² · Volumen 0,0144 m³ · Bearbeitete Kante 0 m	1	Stk

Mengen entstehen aus dieser Revision. Kein pauschaler Verschnitt, keine erfundenen Einkaufsdaten, keine Gewichtsannahme ohne belegte Materialdichte. Modellierte Ausschnitte werden explizit abgezogen. Flächenregeln für die Abrechnung separat fachlich bestätigen.

Modellhash 54e80a856ce3bda9459534e770f988db91b14ffeafff3fedc5e4f4b7428a922c

Entwurf · Intern · Revision 3

- „UX Nachtest planner_a · Innenraum · Wand 1“: Dieses Maß (2500 mm) ist als Planmaß eingetragen, aber noch nicht fachlich bestätigt.
- „UX Nachtest planner_a · Innenraum · Wand 1“: Dieses Maß (150 mm) ist als Planmaß eingetragen, aber noch nicht fachlich bestätigt.
- „UX Nachtest planner_a · Innenraum · Wand 2“: Dieses Maß (2500 mm) ist als Planmaß eingetragen, aber noch nicht fachlich bestätigt.
- „UX Nachtest planner_a · Innenraum · Wand 2“: Dieses Maß (150 mm) ist als Planmaß eingetragen, aber noch nicht fachlich bestätigt.
- „UX Nachtest planner_a · Innenraum · Wand 3“: Dieses Maß (2500 mm) ist als Planmaß eingetragen, aber noch nicht fachlich bestätigt.
- „UX Nachtest planner_a · Innenraum · Wand 3“: Dieses Maß (150 mm) ist als Planmaß eingetragen, aber noch nicht fachlich bestätigt.
- „UX Nachtest planner_a · Innenraum · Wand 4“: Dieses Maß (2500 mm) ist als Planmaß eingetragen, aber noch nicht fachlich bestätigt.
- „UX Nachtest planner_a · Innenraum · Wand 4“: Dieses Maß (150 mm) ist als Planmaß eingetragen, aber noch nicht fachlich bestätigt.
- „UX Nachtest planner_a · Innenraum“: Dieses Maß (0 mm) ist als Planmaß eingetragen, aber noch nicht fachlich bestätigt.
- „UX Nachtest planner_a · Waschtisch · Länge“: Breite (1200 mm) ist als Planmaß eingetragen, aber noch nicht fachlich bestätigt.
- „UX Nachtest planner_a · Waschtisch · Tiefe“: Höhen- / Längenmaß (600 mm) ist als Planmaß eingetragen, aber noch nicht fachlich bestätigt.
- „UX Nachtest planner_a · Waschtisch“: Stärke (20 mm) ist als Planmaß eingetragen, aber noch nicht fachlich bestätigt.
- „UX Nachtest planner_a · Waschtisch“: vorgesehenes Rohmaß oder konkrete Rohplatte und Zuschnittbezug sind noch offen.
- Geometrieprüfung ersetzt keine Prüfung von Untergrund, Abdichtung, Materialeignung, Lasten oder Einbausituation.

Modellhash 54e80a856ce3bda9459534e770f988db91b14ffeafff3fedc5e4f4b7428a922c