Grundriss / Draufsicht

Synthetische Studio-QA Raum

Entwurf · Intern · Revision 117

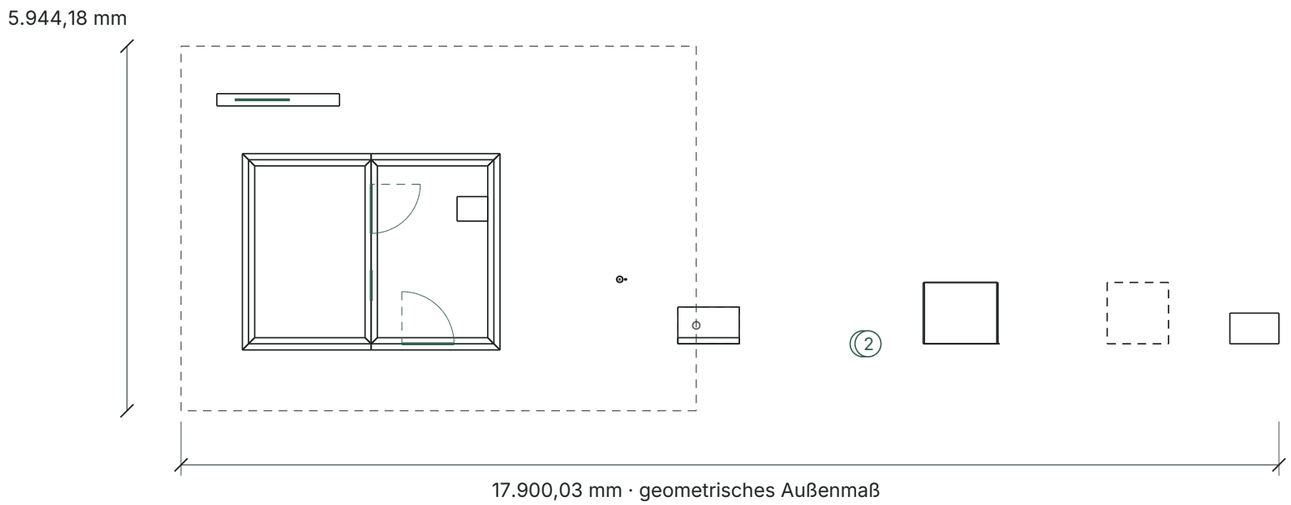

1.411,11 mm · Maßstab 1:100

Höhenbezug: Planursprung · Höhenbezug noch zu bestätigen

Maßhaltige Bauteilgeometrie. Schrift wird hier nicht durch ähnliche Zeichensätze ersetzt. Wörtlicher Text und Herstellerreferenz stehen im Inschriftenplan. Speicherpräzision 0,01 mm ist keine Fertigungstoleranz.

Vorderansicht

Synthetische Studio-QA Raum

Entwurf · Intern · Revision 117

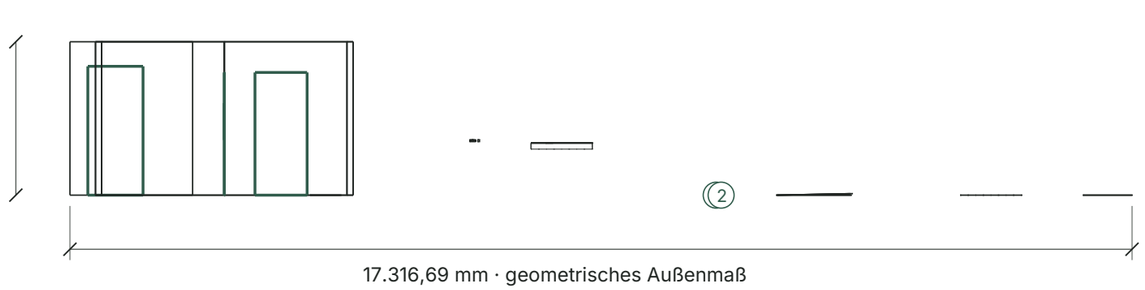

1.411,11 mm · Maßstab 1:100

Höhenbezug: Planursprung · Höhenbezug noch zu bestätigen

Maßhaltige Bauteilgeometrie. Schrift wird hier nicht durch ähnliche Zeichensätze ersetzt. Wörtlicher Text und Herstellerreferenz stehen im Inschriftenplan. Speicherpräzision 0,01 mm ist keine Fertigungstoleranz.

Modellhash a37c3b1c6f74ff1773bf5499ad2f2dad48a33c8309c28324578b1160aee288e0

Seitenansicht

Synthetische Studio-QA Raum

Entwurf · Intern · Revision 117

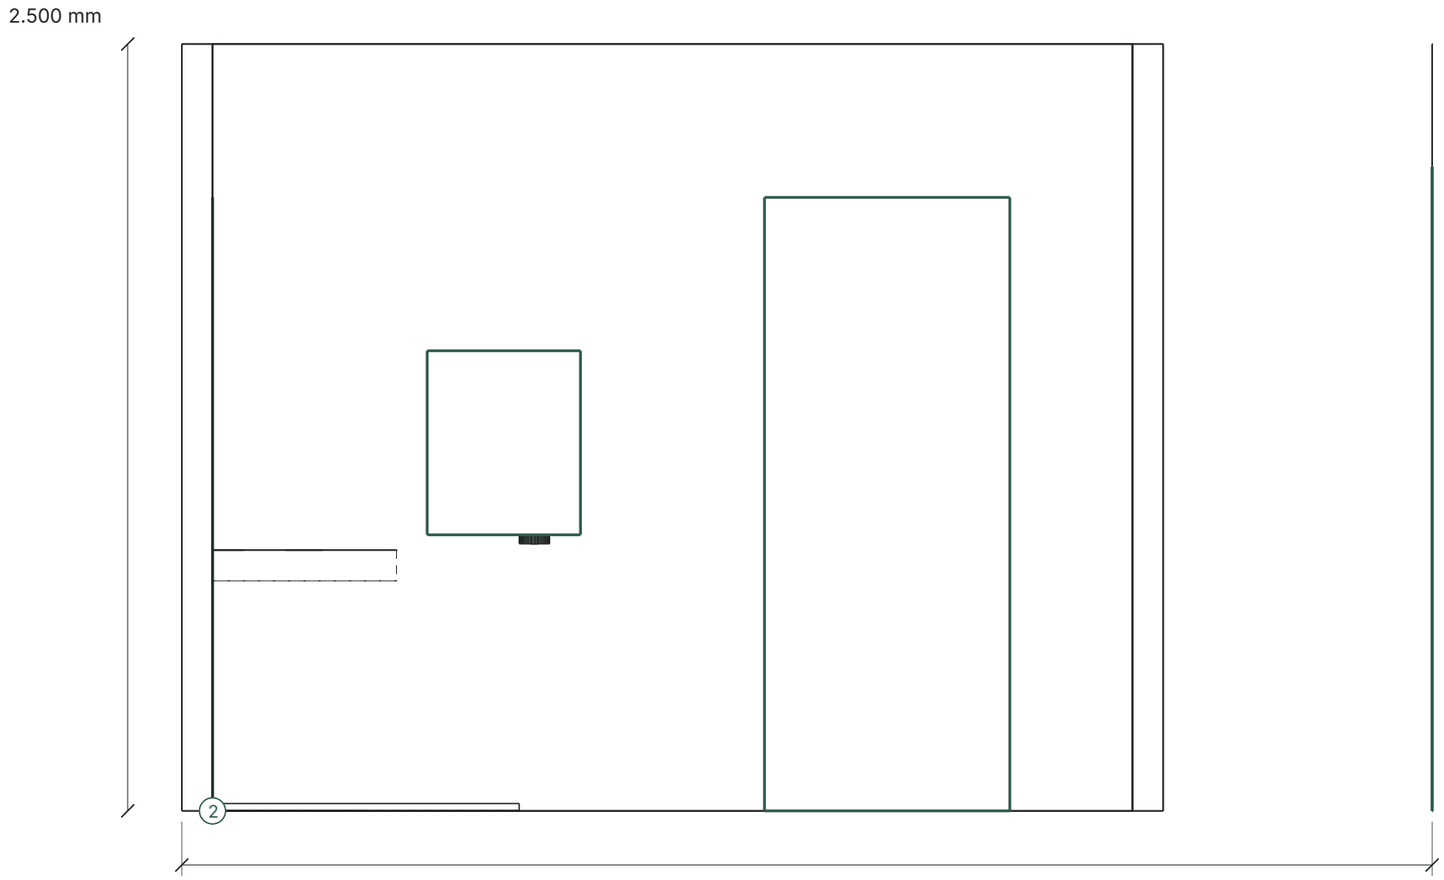

282,22 mm · Maßstab 1:20

Höhenbezug: Planursprung · Höhenbezug noch zu bestätigen

Maßhaltige Bauteilgeometrie. Schrift wird hier nicht durch ähnliche Zeichensätze ersetzt. Wörtlicher Text und Herstellerreferenz stehen im Inschriftenplan. Speicherpräzision 0,01 mm ist keine Fertigungstoleranz.

Modellhash a37c3b1c6f74ff1773bf5499ad2f2dad48a33c8309c28324578b1160aee288e0

Stück- und Bearbeitungsliste

Synthetische Studio-QA Raum

Entwurf · Intern · Revision 117

BAUTEIL / AUSFÜHRUNG	MENGE	EINHEIT
Synthetischer Raum 2 × 3 m · Wand 1 Wand · Stärke 200 mm · Netto 3.3 m² · Volumen 0.6475 m³	2	m
Synthetischer Raum 2 × 3 m · Wand 2 Wand · Stärke 200 mm · Netto 7.5 m² · Volumen 1.5 m³	3	m
Synthetischer Raum 2 × 3 m · Wand 3 Wand · Stärke 200 mm · Netto 5 m² · Volumen 0.9875 m³	2	m
Synthetischer Raum 2 × 3 m · Wand 4 Wand · Stärke 200 mm · Netto 5.9 m² · Volumen 1.112 m³	3	m
Synthetischer Raum 2 × 3 m Raumfläche · Netto 6 m² · Bearbeitete Kante 10 m	6	m²
Synthetisches Hüllmodell Katalogartikel	1	Stk
Import · Wand Wand · Stärke 200 mm · Netto 3.110075 m² · Volumen 0.622015 m³ · Technische Quellen: 045f0e20-d2a5-4ebb-af4e-9b79e95fb1cb	2.00003	m
Synthetische Vektorimport-QA Natursteinbauteil · Materialstand: noch nicht zugeordnet · Stärke 30 mm · Netto 0.00774712 m² · Volumen 0.00023241 m³ · Bearbeitete Kante 0 m · Technische Quellen: a7263e56-f4db-4768-acef-6585614219f7, ef735778-6154-4baa-be26-53f872ff4d26	2	Stk
QA Werkstück Bearbeitung Natursteinbauteil · Materialstand: noch nicht zugeordnet · Stärke 100 mm · Netto 0.6 m² · Volumen 0.05443451 m³ · Bearbeitete Kante 0 m · Rohmaß: 1010 × 620 × 110 mm im lokalen Bauteilbezug; keine automatische Verschnitt-/Nestingregel.	1	Stk
QA Gehrung Vorderkante Bearbeitung · Gehrung · Vorderseite · Tiefe 100 mm · Konturfläche 0.1 m² · Kante 1 · Gehrungswinkel zur Fläche 45°; abgeleitete Kontur auf 0,01 mm quantisiert.	1	Stk

Modellhash a37c3b1c6f74ff1773bf5499ad2f2dad48a33c8309c28324578b1160aee288e0

Stück- und Bearbeitungsliste · Fortsetzung

Synthetische Studio-QA Raum

Entwurf · Intern · Revision 117

BAUTEIL / AUSFÜHRUNG	MENGE	EINHEIT
QA Nebenraum oben Wand · Stärke 200 mm · Netto 5 m² · Volumen 0.9875 m³	2	m
QA Nebenraum West Wand · Stärke 200 mm · Netto 7.5 m² · Volumen 1.5 m³	3	m
QA Nebenraum unten Wand · Stärke 200 mm · Netto 5 m² · Volumen 0.9875 m³	2	m
QA Nebenraum mit gemeinsamer Wand Raumfläche · Netto 6 m² · Bearbeitete Kante 10 m	6	m²
QA Nebenraum mit gemeinsamer Wand · Bodenschicht Schichtaufbau · Materialstand: noch nicht zugeordnet · Stärke 10 mm · Netto 6 m² · Volumen 0.06 m³	6	m²
QA Nebenraum mit gemeinsamer Wand · Bodenschicht Schichtaufbau · Materialstand: noch nicht zugeordnet · Stärke 20 mm · Netto 6 m² · Volumen 0.12 m³	6	m²
QA Belagsfläche Belagsfläche · Netto 1.20023998 m² · Bewegungsfugen: QA Fugenpunkt; Lage und Ausführung gemäß zugeordneten Fachunterlagen.	1.20023998	m²
QA Belagsfläche · Schicht Schichtaufbau · Materialstand: noch nicht zugeordnet · Stärke 15 mm · Netto 1.20023998 m² · Volumen 0.0180036 m³ · Bewegungsfugen: QA Fugenpunkt; Lage und Ausführung gemäß zugeordneten Fachunterlagen.	1.20023998	m²
QA Belagsfläche · Kopie Belagsfläche · Netto 1.2 m²	1.2	m²
QA Belagsfläche · Kopie · Schicht Schichtaufbau · Materialstand: noch nicht zugeordnet · Stärke 15 mm · Netto 1.2 m² · Volumen 0.018 m³	1.2	m²
QA Freizone Freiraumkontrolle · Freiraumkontur 1 m² · Höhe 2000 mm · Der Prüfbereich ist keine abzurechnende Belagsfläche oder Materialmenge.	1	Stk

Modellhash a37c3b1c6f74ff1773bf5499ad2f2dad48a33c8309c28324578b1160aee288e0

Stück- und Bearbeitungsliste · Fortsetzung

Synthetische Studio-QA Raum

Entwurf · Intern · Revision 117

BAUTEIL / AUSFÜHRUNG	MENGE	EINHEIT
QA Blindbohrung Bearbeitung · Bohrung · Vorderseite · Tiefe 50 mm · Konturfläche 0.01130973 m²	1	Stk
QA Fugenpunkt Anschlusspunkt · Art: Fuge / Anschluss · Durchmesser offen mm · Bezug: QA Werkstück Bearbeitung · Ein modellierter Prüf-/Anschlusspunkt; keine automatische Material-, Befestiger- oder Leitungsmenge.	1	Stk
QA Fläche mit Anfangsstärke Belagsfläche · Netto 0.4 m²	0.4	m²
QA Fläche mit Anfangsstärke · Schicht Schichtaufbau · Materialstand: noch nicht zugeordnet · Stärke 18 mm · Netto 0.4 m² · Volumen 0.0072 m³	0.4	m²
QA Gefälle Belag Gefällevorgabe · Höhenunterschied 25 mm · horizontale Länge 1250 mm · 2 % · Bezug: QA Belagsfläche · Aus der ausdrücklich modellierten Ebene abgeleitet; keine automatische Gefälle- oder Abrechnungsnorm.	1	Stk

Mengen entstehen aus dieser Revision. Kein pauschaler Verschnitt, keine erfundenen Einkaufsdaten, keine Gewichtsannahme ohne belegte Materialdichte. Modellierte Ausschnitte werden explizit abgezogen. Flächenregeln für die Abrechnung separat fachlich bestätigen.

Modellhash a37c3b1c6f74ff1773bf5499ad2f2dad48a33c8309c28324578b1160aee288e0

Originalversion: 045f0e20-d2a5-4ebb-af4e-9b79e95fb1cb

Original-SHA-256: 5f315fa5a9cb46e6a55b549eba80bc4c123f2d59560327e69bbea18bb7bbad39

Seite 1 · Quelle pdf_plan · 1440 × 1019 Rasterpixel

Vorschauversion: 7df4bc15-c526-4dee-8d46-4e98088bc0f6

Vorschau-SHA-256: 662918e472c1104013a633b92dd85733c27415be6f8f3c578144dc67b3d8d5a2

QUELLENREFERENZ / IMPORTVORSCHLAG: Diese Kalibrierung bestätigt kein Aufmaß. Perspektivische Fotos sind ohne belegte Projektion kein maßhaltiger Grundriss.

Kontrolltoleranz: 0.5 mm; keine Fertigungstoleranz.

X: (531.43, 831.81) bis (908.57, 831.81) px · abgelesen 2200 mm · ungeprüft

Y: (501.19, 801.57) bis (501.19, 253.00) px · abgelesen 3200 mm · ungeprüft

CONTROL: (548.57, 784.43) bis (548.57, 270.14) px · abgelesen 3000 mm · ungeprüft

Entwurf · Intern · Revision 117

DXF · 2 getrennte Bestandteile · 1 Innenkonturen

Originalversion: ef735778-6154-4baa-be26-53f872ff4d26

Original-SHA-256: 651662084773bd38c0456b26588fb2c6cfc1200771449fdd960dafae8861f56e

Parser: schubert-vector/1.0.0 · ausdrücklich bestätigte Quelleinheit mm; Zielkoordinaten in mm

Originale Z-Ebene: 0 mm; lokale XY-Kontur ohne Bestätigung einer Einbauhöhe.

Analytische Geraden/Kreisbögen · maximal 0.05 mm Importfehler einschließlich 0,01-mm-Koordinatenquantisierung. Keine Fertigungstoleranz.

FACHLICH UNGEPRÜFTER IMPORTVORSCHLAG. Vor Verwendung zur Fertigung Quelle, Konturrollen, Fehlergrenze und Eignung mit eigenem versioniertem Prüfprotokoll bestätigen.

Nutzungsrechte, Materialeignung und Freigabe dieser Gesamtplanrevision werden separat nachgewiesen.

- „Synthetischer Raum 2 × 3 m · Wand 1“: 86616276-ba19-4d51-9ad4-c5263c34cbc6:wall-height ist noch nicht festgelegt.
- „Synthetischer Raum 2 × 3 m · Wand 1“: 86616276-ba19-4d51-9ad4-c5263c34cbc6:wall-core ist noch nicht festgelegt.
- „Synthetischer Raum 2 × 3 m · Wand 2“: 86616276-ba19-4d51-9ad4-c5263c34cbc6:wall-height ist noch nicht festgelegt.
- „Synthetischer Raum 2 × 3 m · Wand 2“: 86616276-ba19-4d51-9ad4-c5263c34cbc6:wall-core ist noch nicht festgelegt.
- „Synthetischer Raum 2 × 3 m · Wand 3“: 86616276-ba19-4d51-9ad4-c5263c34cbc6:wall-height ist noch nicht festgelegt.
- „Synthetischer Raum 2 × 3 m · Wand 3“: 86616276-ba19-4d51-9ad4-c5263c34cbc6:wall-core ist noch nicht festgelegt.
- „Synthetischer Raum 2 × 3 m · Wand 4“: 86616276-ba19-4d51-9ad4-c5263c34cbc6:wall-height ist noch nicht festgelegt.
- „Synthetischer Raum 2 × 3 m · Wand 4“: 86616276-ba19-4d51-9ad4-c5263c34cbc6:wall-core ist noch nicht festgelegt.
- „Synthetischer Raum 2 × 3 m“: 86616276-ba19-4d51-9ad4-c5263c34cbc6:floor-level ist noch nicht festgelegt.
- „Synthetische Tür“: 0419829b-10c2-4bd2-a4bc-beb90aaf981b:width ist noch nicht festgelegt.
- „Synthetische Tür“: 0419829b-10c2-4bd2-a4bc-beb90aaf981b:height ist noch nicht festgelegt.
- „Synthetische Tür“: 0419829b-10c2-4bd2-a4bc-beb90aaf981b:offset ist noch nicht festgelegt.
- „Synthetische Tür“: 0419829b-10c2-4bd2-a4bc-beb90aaf981b:sill ist noch nicht festgelegt.
- „Synthetisches Hüllmodell“: freies Hüllmodell ohne bestellbare Produktvariante.
- „Synthetisches Hüllmodell“: ddbdb995-5c19-43b4-9e17-81b365c86ff3:envelope-height ist noch nicht festgelegt.
- „Synthetisches Hüllmodell“: Darstellung vereinfacht; Produktgeometrie nicht verifiziert.
- „Import · Wand“: 7d463a13-c1e7-4ba0-8977-a06c31fa68e8 ist geschätzt.
- „Import · Wand“: 7d463a13-c1e7-4ba0-8977-a06c31fa68e8 ist noch nicht festgelegt.

- „Import · Wand“: 842a039b-aa13-4df9-8ef7-2234f1655cb9 ist geschätzt.
- „Import · Wand“: 842a039b-aa13-4df9-8ef7-2234f1655cb9 ist noch nicht festgelegt.
- „Import · ungeprüfte Wandlänge“: b9252bb0-2cdb-4b85-87a5-87886fef95d2 ist geschätzt.
- „Import · ungeprüfte Wandlänge“: b9252bb0-2cdb-4b85-87a5-87886fef95d2 ist noch nicht festgelegt.
- „Import · Öffnung“: a42ba616-a37a-41df-8931-aa100f5febd0 ist geschätzt.
- „Import · Öffnung“: a42ba616-a37a-41df-8931-aa100f5febd0 ist noch nicht festgelegt.
- „Import · Öffnung“: 07860409-a3f3-4a7e-9192-30247f5326cc ist geschätzt.
- „Import · Öffnung“: 07860409-a3f3-4a7e-9192-30247f5326cc ist noch nicht festgelegt.
- „Import · Öffnung“: 1e7e16ba-1b34-43d2-af72-25e5dd2ae8d2 ist geschätzt.
- „Import · Öffnung“: 1e7e16ba-1b34-43d2-af72-25e5dd2ae8d2 ist noch nicht festgelegt.
- „Import · Öffnung“: 897541f8-c7f0-4a09-bb7b-22baf5fe8fae ist geschätzt.
- „Import · Öffnung“: 897541f8-c7f0-4a09-bb7b-22baf5fe8fae ist noch nicht festgelegt.
- „Quelle: 3.200“: 24700e2d-bed5-43a7-9d65-dc81cdb8ab35 ist geschätzt.
- „Quelle: 3.200“: 24700e2d-bed5-43a7-9d65-dc81cdb8ab35 ist noch nicht festgelegt.
- „Synthetische Vektorimport-QA · Breite“: de1b3dba-7807-4574-bfa8-c05dcb61cbda:width ist noch nicht festgelegt.
- „Synthetische Vektorimport-QA · Höhe / Länge“: de1b3dba-7807-4574-bfa8-c05dcb61cbda:height ist noch nicht festgelegt.
- „Synthetische Vektorimport-QA“: Importkontur mit Fehlergrenze 0.05 mm ist noch nicht fachlich bestätigt.
- „Synthetische Vektorimport-QA“: konkrete Materialversion fehlt.
- „Synthetische Vektorimport-QA“: de1b3dba-7807-4574-bfa8-c05dcb61cbda:thickness ist noch nicht festgelegt.
- „Synthetische Vektorimport-QA“: vorgesehenes Rohmaß oder konkrete Rohplatte und Zuschnittbezug sind noch offen.
- „QA Werkstück Bearbeitung · Breite“: 2120d396-8794-4cbe-882b-17217dc98ff4:width ist noch nicht festgelegt.

- „QA Werkstück Bearbeitung · Höhe / Länge“: 2120d396-8794-4cbe-882b-17217dc98ff4:height ist noch nicht festgelegt.
- „QA Werkstück Bearbeitung“: konkrete Materialversion fehlt.
- „QA Werkstück Bearbeitung“: 2120d396-8794-4cbe-882b-17217dc98ff4:thickness ist noch nicht festgelegt.
- „QA Werkstück Bearbeitung“: e938e7ce-4dbc-41b1-939d-3c624a6bc227 ist noch nicht festgelegt.
- „QA Werkstück Bearbeitung“: c66ae4c2-e931-4fe3-b78d-d2be75c2e687 ist noch nicht festgelegt.
- „QA Werkstück Bearbeitung“: 6e05d6ae-1f70-4167-a526-3c2d4a372bb8 ist noch nicht festgelegt.
- „QA Gehrung Vorderkante“: db43da50-f470-4d23-82a7-2cc84986f06d:minimum-web ist noch nicht festgelegt.
- „QA Nebenraum oben“: f226df40-691d-4196-9169-9e0943ece2eb:height ist noch nicht festgelegt.
- „QA Nebenraum oben“: f226df40-691d-4196-9169-9e0943ece2eb:core ist noch nicht festgelegt.
- „QA Nebenraum West“: d85c54b2-c348-4574-b441-b83b451edd02:height ist noch nicht festgelegt.
- „QA Nebenraum West“: d85c54b2-c348-4574-b441-b83b451edd02:core ist noch nicht festgelegt.
- „QA Nebenraum unten“: 1db3544f-cba0-4b08-891d-a5e483c2e260:height ist noch nicht festgelegt.
- „QA Nebenraum unten“: 1db3544f-cba0-4b08-891d-a5e483c2e260:core ist noch nicht festgelegt.
- „QA Nebenraum mit gemeinsamer Wand“: 80aa5fc0-8e43-4c56-8bba-60f1f9b9cbde:floor-level ist noch nicht festgelegt.
- „QA Nebenraum mit gemeinsamer Wand“: e9cde9b5-fa43-43c9-abb5-0083efe2be2e:thickness ist noch nicht festgelegt.
- „QA Nebenraum mit gemeinsamer Wand“: 181e029e-fa78-4b65-93aa-bacceb239f17:thickness ist noch nicht festgelegt.
- „QA Nische mit Rücken“: c8b2793f-81e4-4aa1-a627-bc05ec4f3e65:width ist noch nicht festgelegt.
- „QA Nische mit Rücken“: c8b2793f-81e4-4aa1-a627-bc05ec4f3e65:height ist noch nicht festgelegt.
- „QA Nische mit Rücken“: c8b2793f-81e4-4aa1-a627-bc05ec4f3e65:offset ist noch nicht festgelegt.
- „QA Nische mit Rücken“: c8b2793f-81e4-4aa1-a627-bc05ec4f3e65:sill ist noch nicht festgelegt.

- „QA Nische mit Rücken“: c8b2793f-81e4-4aa1-a627-bc05ec4f3e65:recess-depth ist noch nicht festgelegt.
- „QA Tür in gemeinsamer Wand“: 456da51c-7c32-4eb1-8cff-8d0b07455e7a:width ist noch nicht festgelegt.
- „QA Tür in gemeinsamer Wand“: 456da51c-7c32-4eb1-8cff-8d0b07455e7a:height ist noch nicht festgelegt.
- „QA Tür in gemeinsamer Wand“: 456da51c-7c32-4eb1-8cff-8d0b07455e7a:offset ist noch nicht festgelegt.
- „QA Tür in gemeinsamer Wand“: 456da51c-7c32-4eb1-8cff-8d0b07455e7a:sill ist noch nicht festgelegt.
- „QA Belagsfläche“: 3c272be8-82e1-4e3e-a5f6-786522b536ac:thickness ist noch nicht festgelegt.
- „QA Belagsfläche“: bestätigter Untergrundmaterialstand fehlt.
- „QA Belagsfläche“: fachliche Aufbau-/Flächenregel noch offen.
- „QA Belagsfläche · Kopie“: 75a0fc0c-ca63-4eee-841c-80b8b78fa6a5:m:0 ist noch nicht festgelegt.
- „QA Belagsfläche · Kopie“: bestätigter Untergrundmaterialstand fehlt.
- „QA Belagsfläche · Kopie“: fachliche Aufbau-/Flächenregel noch offen.
- „QA Freizone“: bestätigte Freiraum-/Einbauregel noch offen.
- „QA Blindbohrung“: 143325e7-d1b2-4872-b4a0-622f7fe91429:machining-depth ist noch nicht festgelegt.
- „QA Blindbohrung“: 143325e7-d1b2-4872-b4a0-622f7fe91429:minimum-web ist noch nicht festgelegt.
- „QA Blindbohrung“: keine bestätigten Befestigungsdaten; keine Bohrschablone freigeben.
- „QA Fugenpunkt“: fachliche Anschluss-/Ausführungsreferenz noch offen.
- „QA Fläche mit Anfangsstärke“: 2bda3b66-d105-4676-85f3-c30caa143649:layer ist noch nicht festgelegt.
- „QA Fläche mit Anfangsstärke“: bestätigter Untergrundmaterialstand fehlt.
- „QA Fläche mit Anfangsstärke“: fachliche Aufbau-/Flächenregel noch offen.
- „QA Gefälle Belag“: e190926f-dbe7-45af-a886-944fdb878d55:rise ist noch nicht festgelegt.
- „QA Gefälle Belag“: e190926f-dbe7-45af-a886-944fdb878d55:run ist noch nicht festgelegt.
- „QA Gefälle Belag“: Gefälle ohne bestätigte Ausführungsregel.

Entwurf · Intern · Revision 117

- Bindung 24be5a0c-16c0-458d-9426-910c90fbe522: Das gebundene Maß ist noch nicht fachlich festgelegt.
- „Synthetische Quellplan-Kalibrierung“: versionierte Quellenreferenz; Kalibrierung und erkannte Maße bleiben ungeprüfte Importdaten.
- „Synthetische Vektorimport-QA“: DXF-Original mit quantisierten Geraden/Kreisbögen; maximal 0.05 mm Importfehler, keine automatische Herstellerfreigabe.
- Geometrieprüfung ersetzt keine Prüfung von Standsicherheit, Verankerung, Abdichtung, Materialeignung, Lasten oder Friedhofsvorgaben.