Grundriss / Draufsicht

Abnahme Bad f4f1cd56

Entwurf · Intern · Revision 2

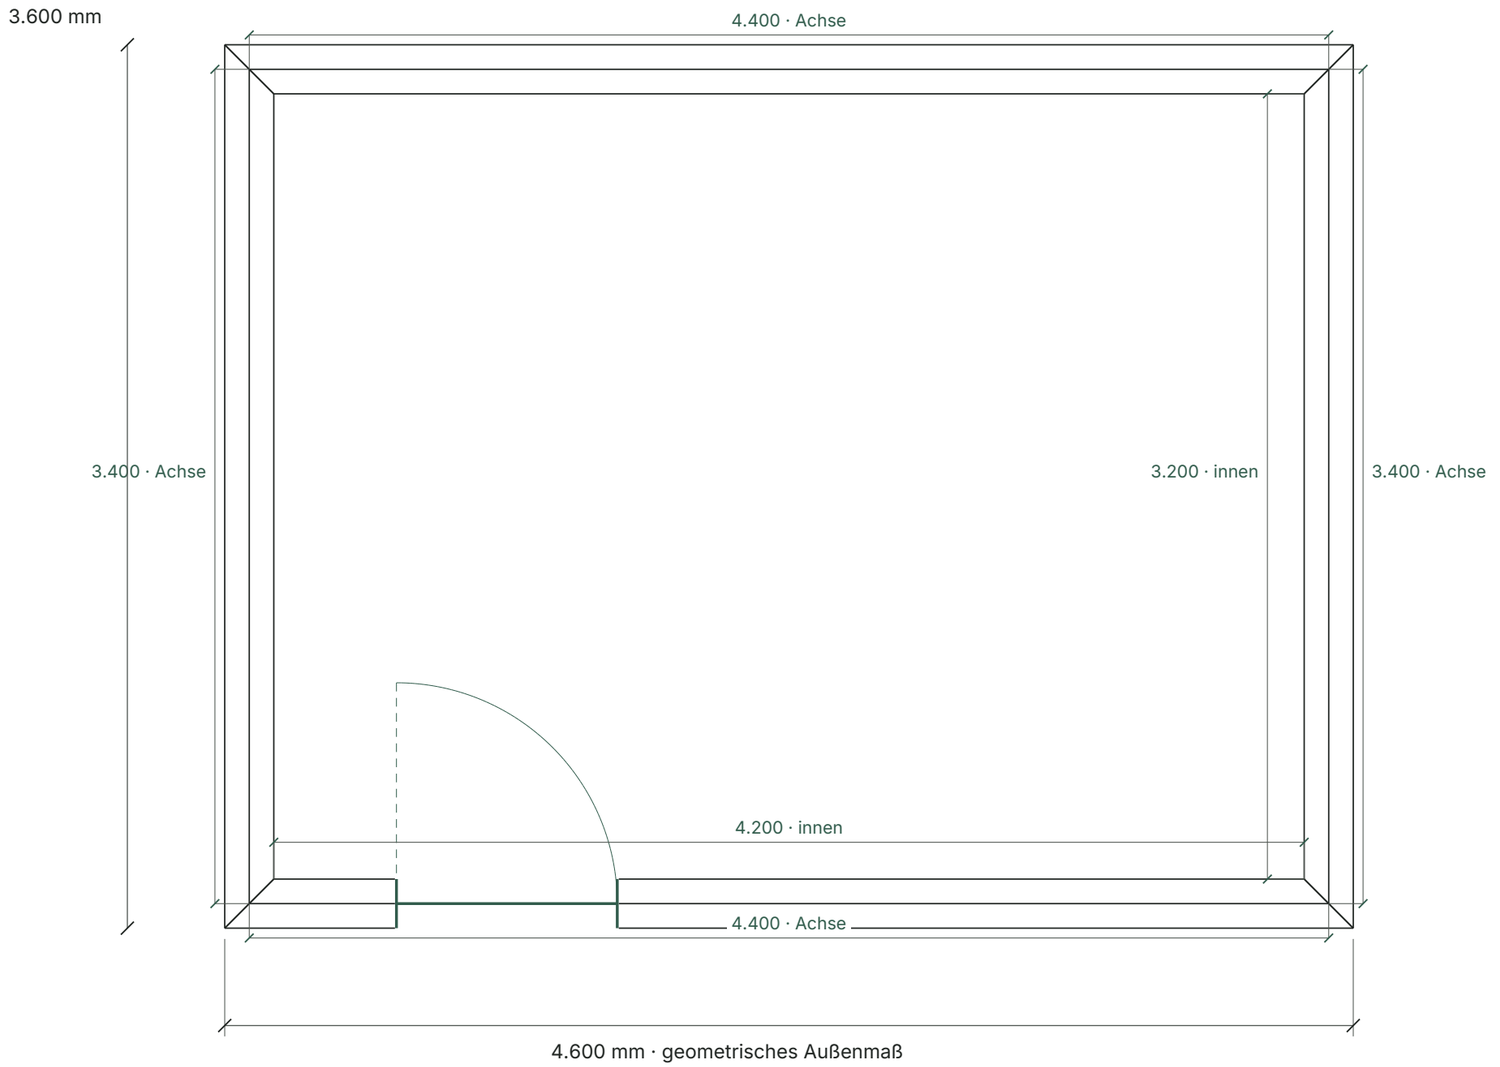

352,78 mm · Maßstab 1:25

Höhenbezug: Planursprung · Höhenbezug noch zu bestätigen

Maße in mm. „Achse“ bezeichnet die Wandachse; „innen“ das modellierte lichte Innenmaß. Planmaße sind kein bestätigtes Aufmaß. Wandaufbau und Einbaumaße vor Ort prüfen. Speicherpräzision 0,01 mm ist keine Fertigungstoleranz.

Modellhash ff040579caaed18c8001c9ab68eee4214d32843b24515885788ab2b75d34d258

Vorderansicht

Abnahme Bad f4f1cd56

Entwurf · Intern · Revision 2

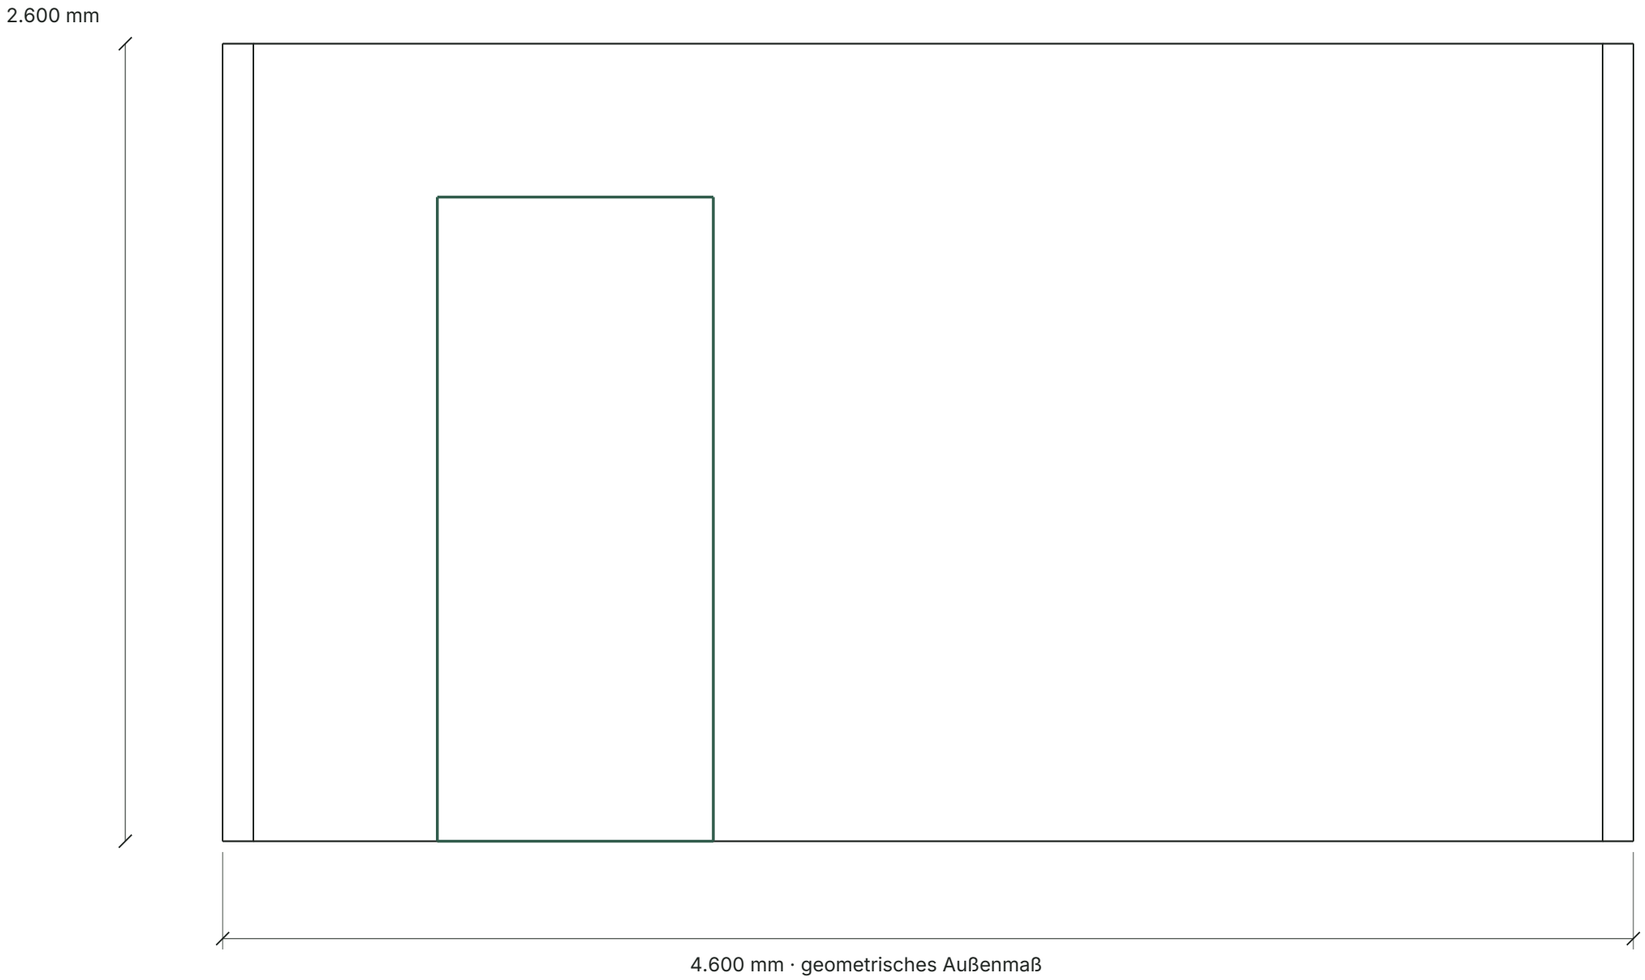

282,22 mm · Maßstab 1:20

Höhenbezug: Planursprung · Höhenbezug noch zu bestätigen

Maße in mm. „Achse“ bezeichnet die Wandachse; „innen“ das modellierte lichte Innenmaß. Planmaße sind kein bestätigtes Aufmaß. Wandaufbau und Einbaumaße vor Ort prüfen. Speicherpräzision 0,01 mm ist keine Fertigungstoleranz.

Seitenansicht

Abnahme Bad f4f1cd56

Entwurf · Intern · Revision 2

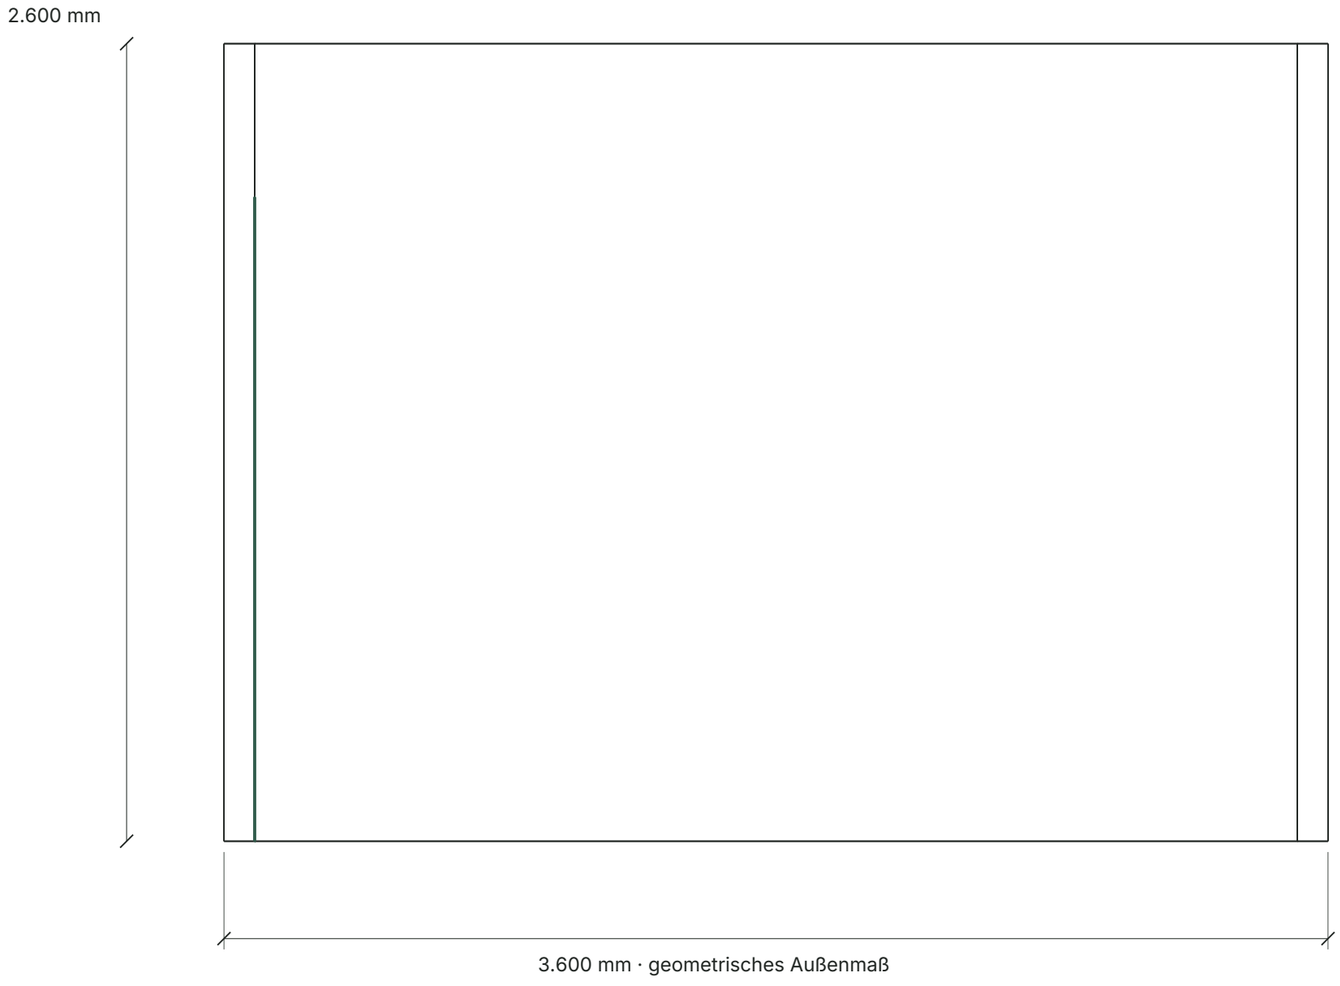

282,22 mm · Maßstab 1:20

Höhenbezug: Planursprung · Höhenbezug noch zu bestätigen

Maße in mm. „Achse“ bezeichnet die Wandachse; „innen“ das modellierte lichte Innenmaß. Planmaße sind kein bestätigtes Aufmaß. Wandaufbau und Einbaumaße vor Ort prüfen. Speicherpräzision 0,01 mm ist keine Fertigungstoleranz.

Modellhash ff040579caaed18c8001c9ab68eee4214d32843b24515885788ab2b75d34d258

Stück- und Bearbeitungsliste

Abnahme Bad f4f1cd56

Entwurf · Intern · Revision 2

BAUTEIL / AUSFÜHRUNG	MENGE	EINHEIT
Bad · 4200 × 3200 mm Innenmaße · Wand 1 Wand · Stärke 200 mm · Netto 9,55 m² · Volumen 1,91 m³	4,4	m
Bad · 4200 × 3200 mm Innenmaße · Wand 2 Wand · Stärke 200 mm · Netto 8,84 m² · Volumen 1,768 m³	3,4	m
Bad · 4200 × 3200 mm Innenmaße · Wand 3 Wand · Stärke 200 mm · Netto 11,44 m² · Volumen 2,288 m³	4,4	m
Bad · 4200 × 3200 mm Innenmaße · Wand 4 Wand · Stärke 200 mm · Netto 8,84 m² · Volumen 1,768 m³	3,4	m
Bad · 4200 × 3200 mm Innenmaße Raumfläche · Flächenbezug: Wandachsen, kein lichtes Innenmaß · Achsfläche 14,96 m² · Umfang zwischen Wandachsen 15,6 m	14,96	m²

Mengen entstehen aus dieser Revision. Kein pauschaler Verschnitt, keine erfundenen Einkaufsdaten, keine Gewichtsannahme ohne belegte Materialdichte. Modellierte Ausschnitte werden explizit abgezogen. Flächenregeln für die Abrechnung separat fachlich bestätigen.

Modellhash ff040579caaed18c8001c9ab68eee4214d32843b24515885788ab2b75d34d258

Prüfstand und offene Angaben

Abnahme Bad f4f1cd56

Entwurf · Intern · Revision 2

- „Bad · 4200 × 3200 mm Innenmaße · Wand 1“: Dieses Maß (2600 mm) ist als Planmaß eingetragen, aber noch nicht fachlich bestätigt.
- „Bad · 4200 × 3200 mm Innenmaße · Wand 1“: Dieses Maß (200 mm) ist als Planmaß eingetragen, aber noch nicht fachlich bestätigt.
- „Bad · 4200 × 3200 mm Innenmaße · Wand 2“: Dieses Maß (2600 mm) ist als Planmaß eingetragen, aber noch nicht fachlich bestätigt.
- „Bad · 4200 × 3200 mm Innenmaße · Wand 2“: Dieses Maß (200 mm) ist als Planmaß eingetragen, aber noch nicht fachlich bestätigt.
- „Bad · 4200 × 3200 mm Innenmaße · Wand 3“: Dieses Maß (2600 mm) ist als Planmaß eingetragen, aber noch nicht fachlich bestätigt.
- „Bad · 4200 × 3200 mm Innenmaße · Wand 3“: Dieses Maß (200 mm) ist als Planmaß eingetragen, aber noch nicht fachlich bestätigt.
- „Bad · 4200 × 3200 mm Innenmaße · Wand 4“: Dieses Maß (2600 mm) ist als Planmaß eingetragen, aber noch nicht fachlich bestätigt.
- „Bad · 4200 × 3200 mm Innenmaße · Wand 4“: Dieses Maß (200 mm) ist als Planmaß eingetragen, aber noch nicht fachlich bestätigt.
- „Bad · 4200 × 3200 mm Innenmaße“: Dieses Maß (0 mm) ist als Planmaß eingetragen, aber noch nicht fachlich bestätigt.
- „Tür · 900 × 2100 mm“: Breite (900 mm) ist als Planmaß eingetragen, aber noch nicht fachlich bestätigt.
- „Tür · 900 × 2100 mm“: Höhe (2100 mm) ist als Planmaß eingetragen, aber noch nicht fachlich bestätigt.
- „Tür · 900 × 2100 mm“: Abstand (600 mm) ist als Planmaß eingetragen, aber noch nicht fachlich bestätigt.
- „Tür · 900 × 2100 mm“: Dieses Maß (0 mm) ist als Planmaß eingetragen, aber noch nicht fachlich bestätigt.
- Geometrieprüfung ersetzt keine Prüfung von Untergrund, Abdichtung, Materialeignung, Lasten oder Einbausituation.

Modellhash ff040579caaed18c8001c9ab68eee4214d32843b24515885788ab2b75d34d258